


IP 16PRO MAX

NETWORK 2

DIGITAL BOARD ESQUEMAS DIGITALIZADOS

IPHONE 16 PRO MAX

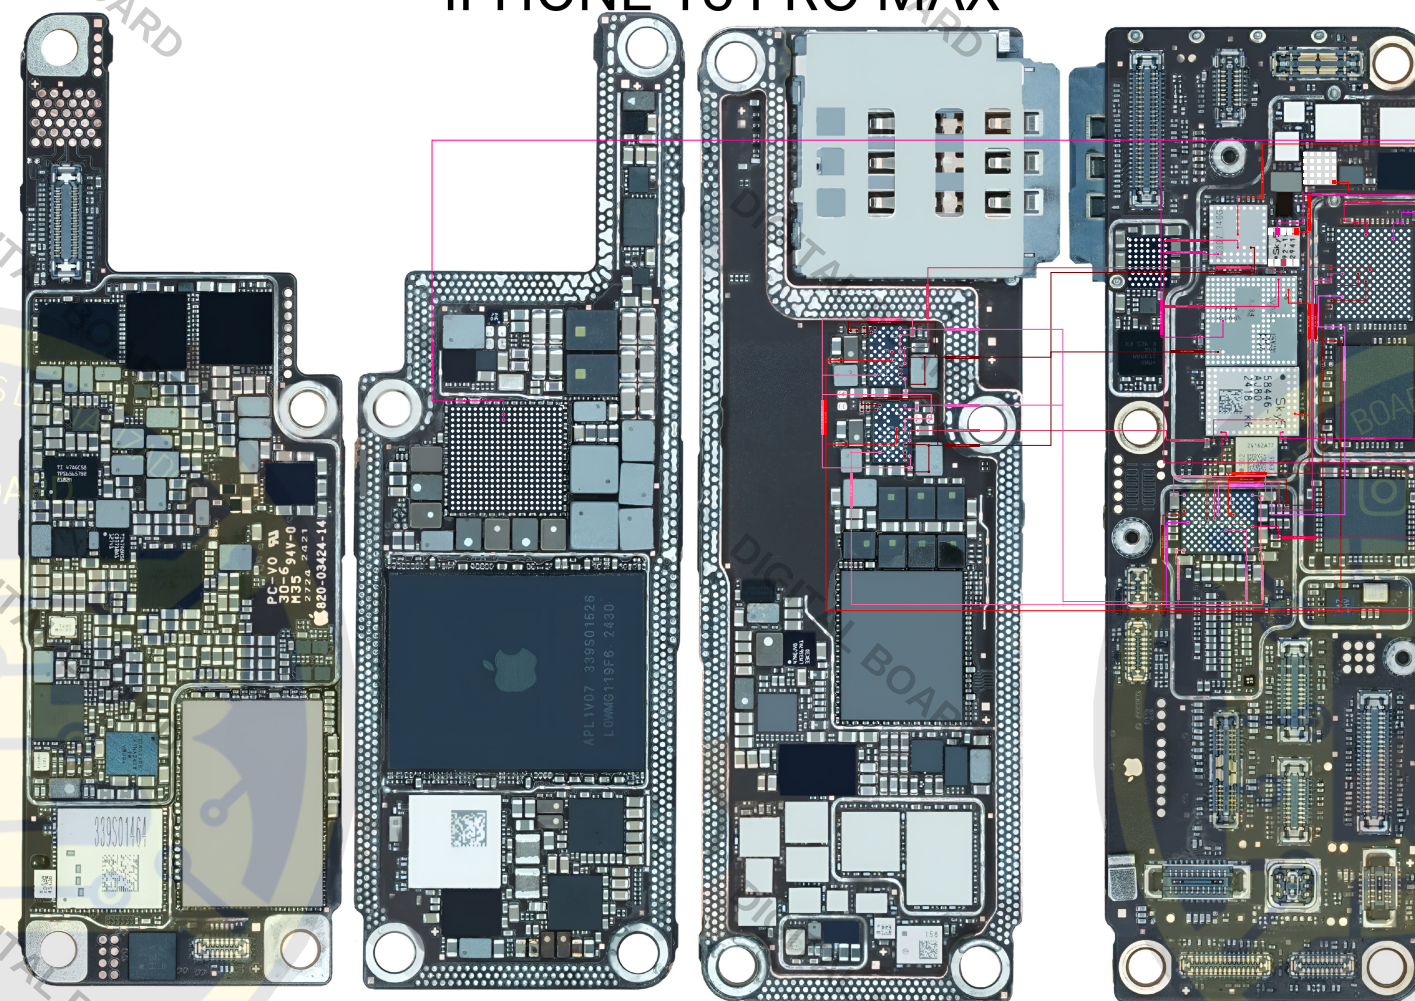

PP_1V2_LDO1	PP_VDD_BOOST
PP_1V8_LDO6	PP_QET0_2G_PA
PP_0V8_LDO8	PP_VDD_MAIN_BBPMU_QET
PP_0V912_LDO20	PP_QET1_ET100
PP_0V912_LDO4	PP_0V8_LDO3
PP_1V776_LDO16	