


IP 8PLUS INT LIGHT

DIGITAL BOARD ESQUEMAS DIGITALIZADOS

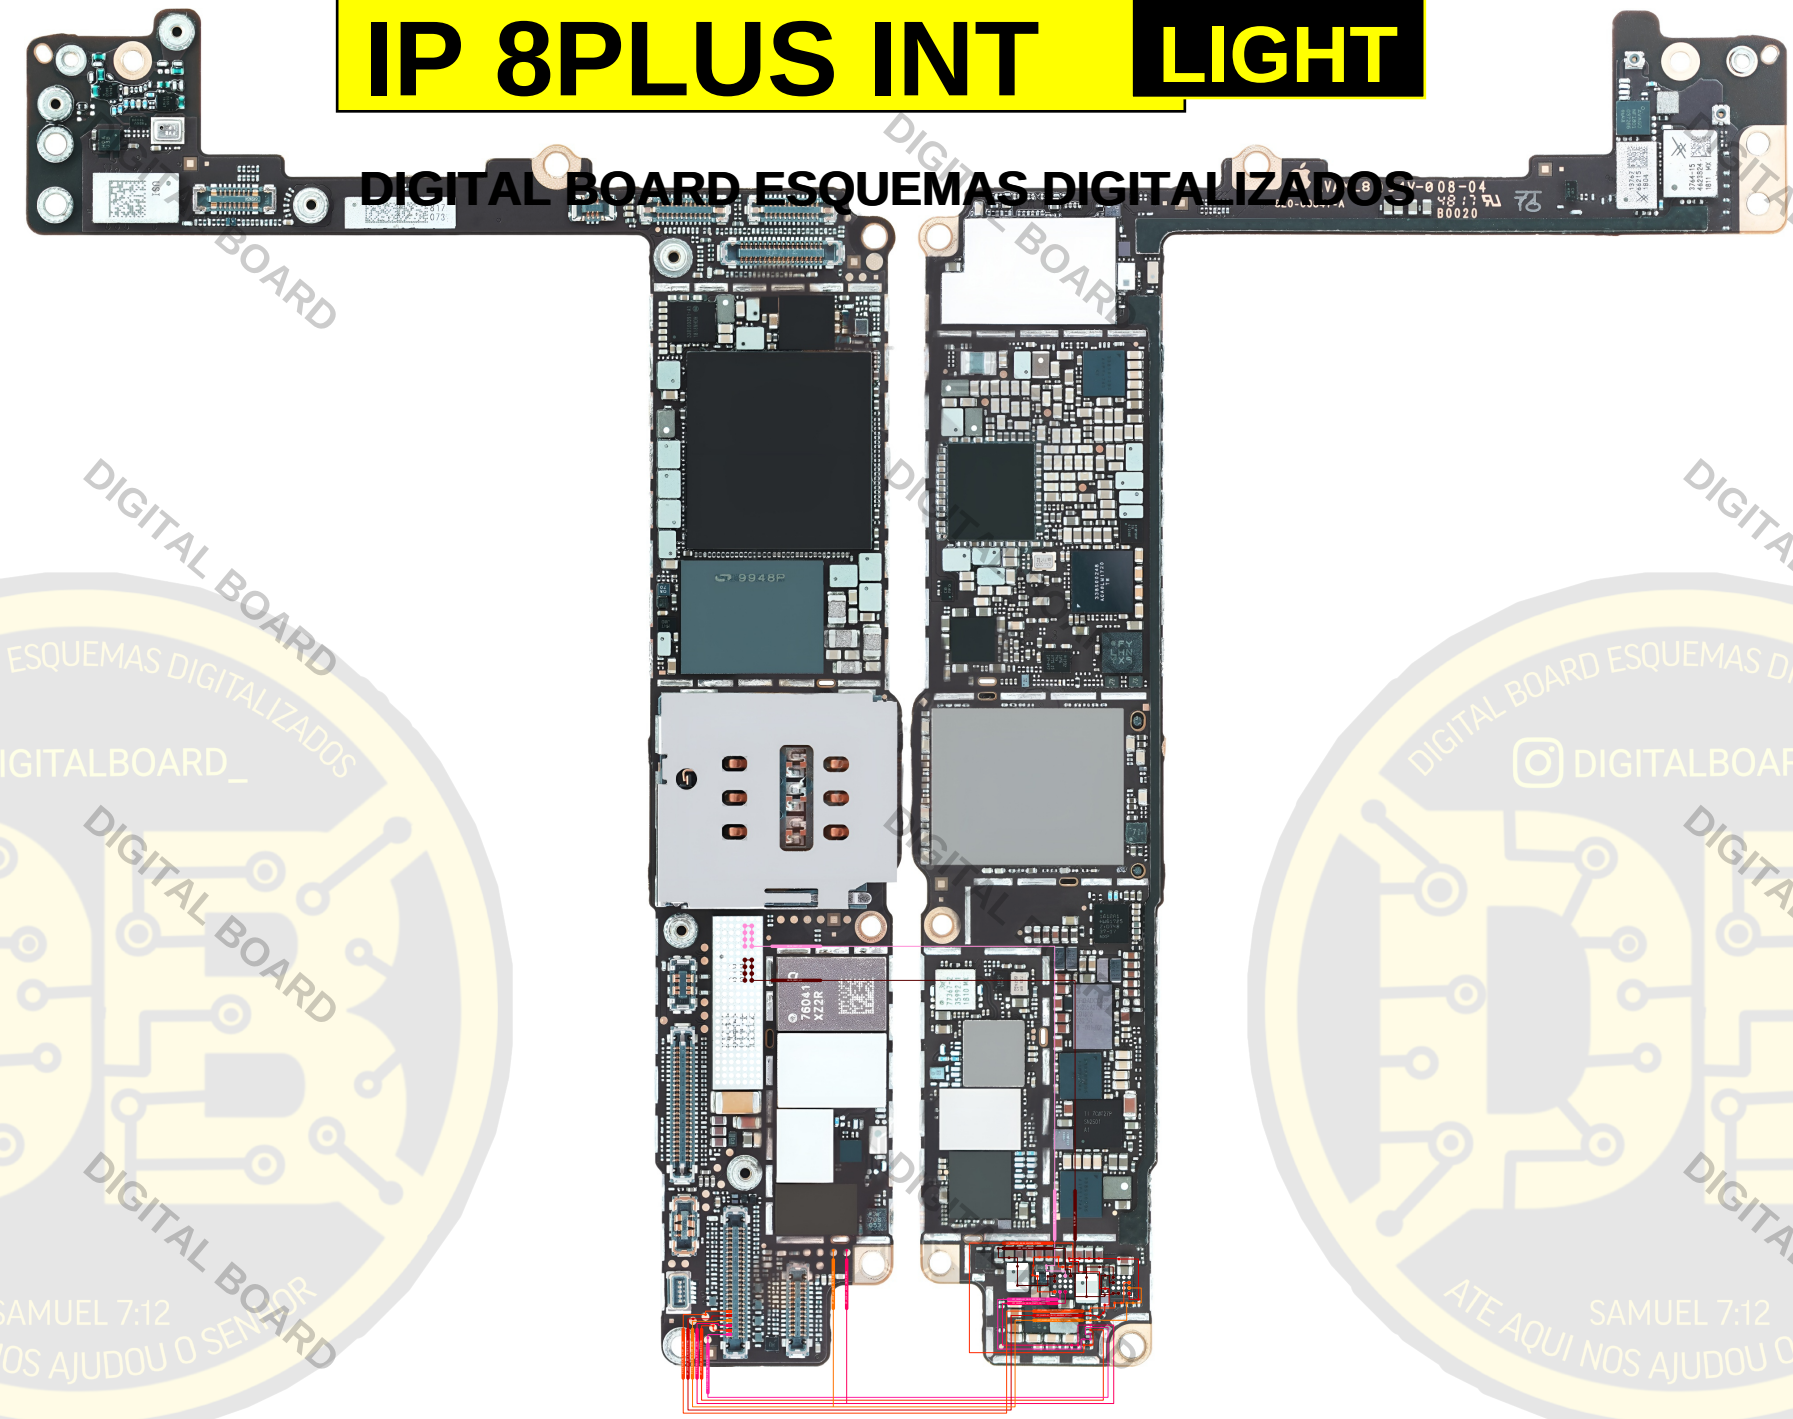

PP_DISPLAY_BL34_ANODE_CONN	BL34_SW1_LX
PP_DISPLAY_BL34_CAT1_CONN	PP_VDD_MAIN
PP_DISPLAY_BL34_CAT2_CONN	
PP_DISPLAY_BL12_ANODE_CONN	
PP_DISPLAY_BL12_CAT1_CONN	
PP_DISPLAY_BL12_CAT2_CONN	