


# IP 16PRO TOF 3D LIDAR

DIGITAL BOARD ESQUEMAS DIGITALIZADOS

IPHONE 16 PRO

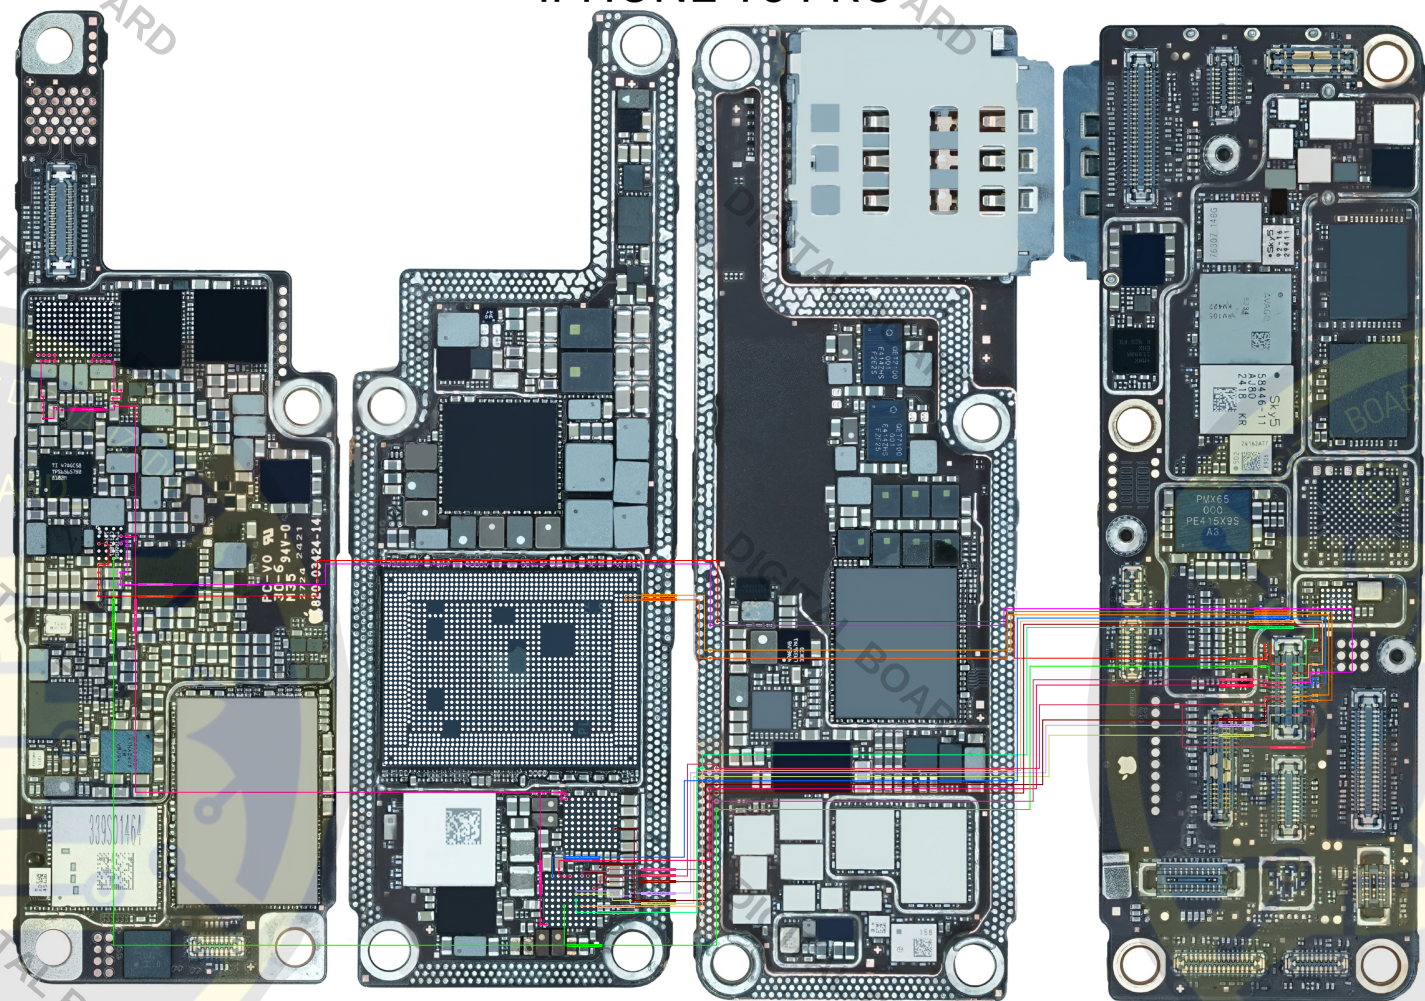

90\_LPDP\_ISP\_FROM\_RDEPTH\_RX\_D0\_CONN\_P  
90\_LPDP\_ISP\_FROM\_RDEPTH\_RX\_D0\_CONN\_N  
GPIO\_CAM\_PMU2\_TO\_RDEPTH\_TX\_CE\_1V8\_CONN  
CLK\_CAM\_PMU2\_TO\_RDEPTH\_12M\_1V8\_CONN  
I2C2\_CAM\_PMU2\_SCL\_1V8\_CONN

GPIO\_CAM\_PMU2\_TO\_RDEPTH\_SHDN\_L\_1V8\_CONN  
GPIO\_CAM\_PMU2\_FROM\_WILL\_RDEPTH\_INT\_L\_1V8  
I2C2\_CAM\_PMU2\_SDA\_1V8\_CONN  
PP\_VDD\_MAIN  
PN\_RDEPTH\_VDDHV\_CONN  
PP\_RDEPTH\_VDDLAS\_CONN

PP1V5\_RDEPTH\_TX\_VDD  
PP3V2\_RDEPTH\_TX\_AVDD  
PP3V0\_RDEPTH\_RX\_AVDD\_CONN  
PP0V9\_RDEPTH\_VDDL2\_CONN  
PP1V8\_RCAM\_VDDIO