


IP 16PRO MAX LCD LIGHT

DIGITAL BOARD ESQUEMAS DIGITALIZADOS
IPHONE 16 PRO MAX

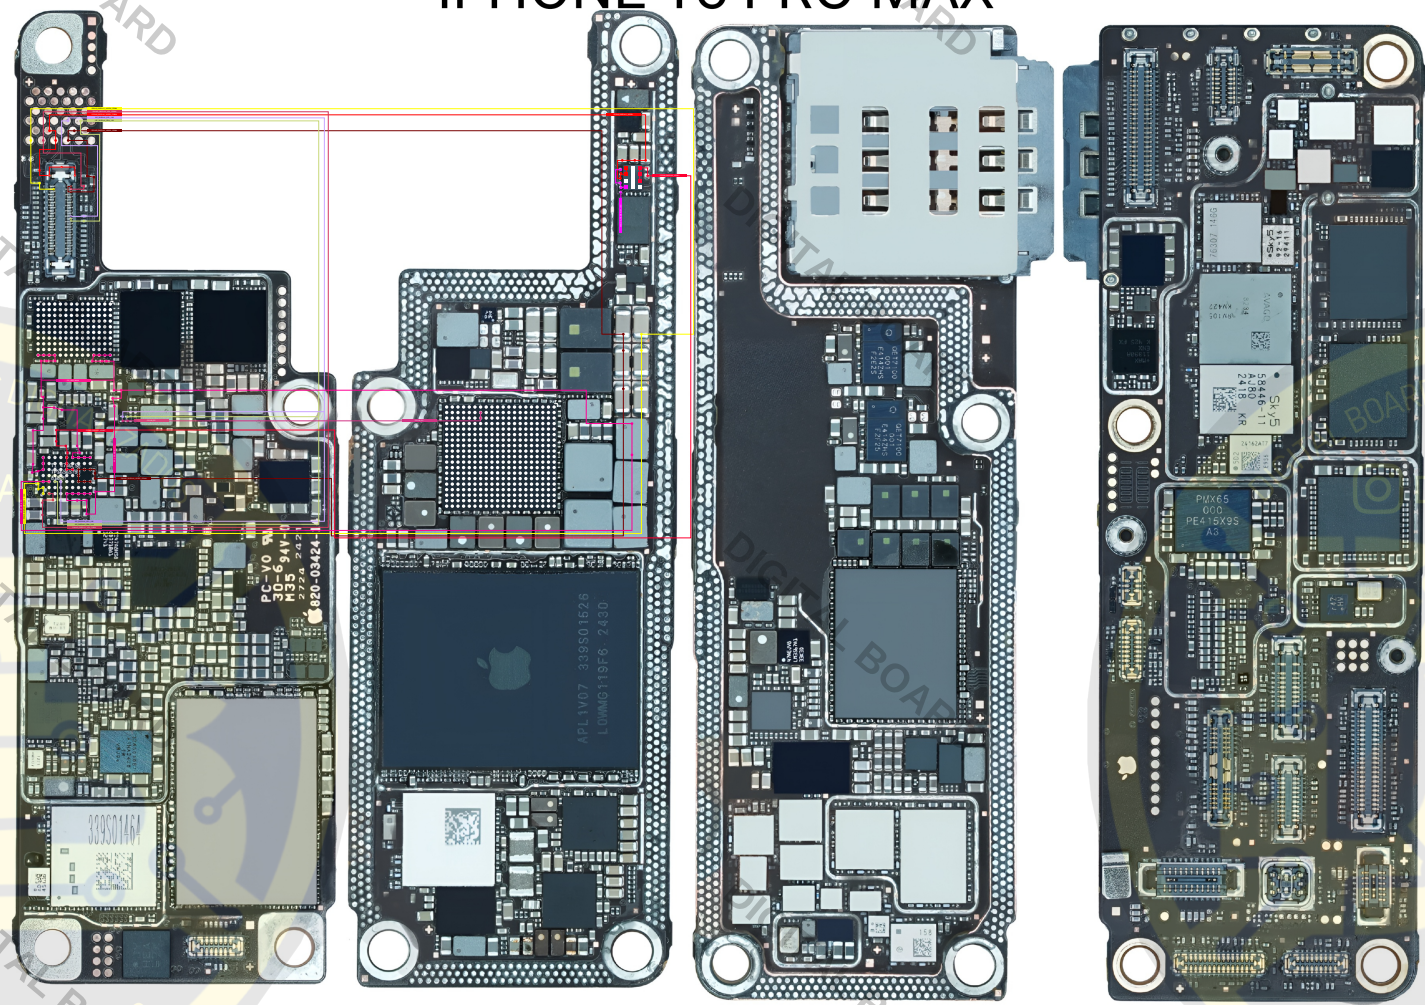

I2C_DISPLAY_SDA_1V8	ANALOG_FB_DISPLAY_LDO
I2C_DISPLAY_SCL_1V8	PPVAR_DISPLAY_VSSEL_CONN
PP6V8_DISPLAY_VDDEL_CONN	PP2V8_DISPLAY_VDDEL_CONN
PNVAR_DISPLAY_VGL_CONN	PP3V0_DISPLAY_VDDEL
PP1V8_S2	PP_VDD_MAIN