


# IP 16PRO MAX CAM ULTRAWIDE

## DIGITAL BOARD ESQUEMAS DIGITALIZADOS IPHONE 16 PRO MAX

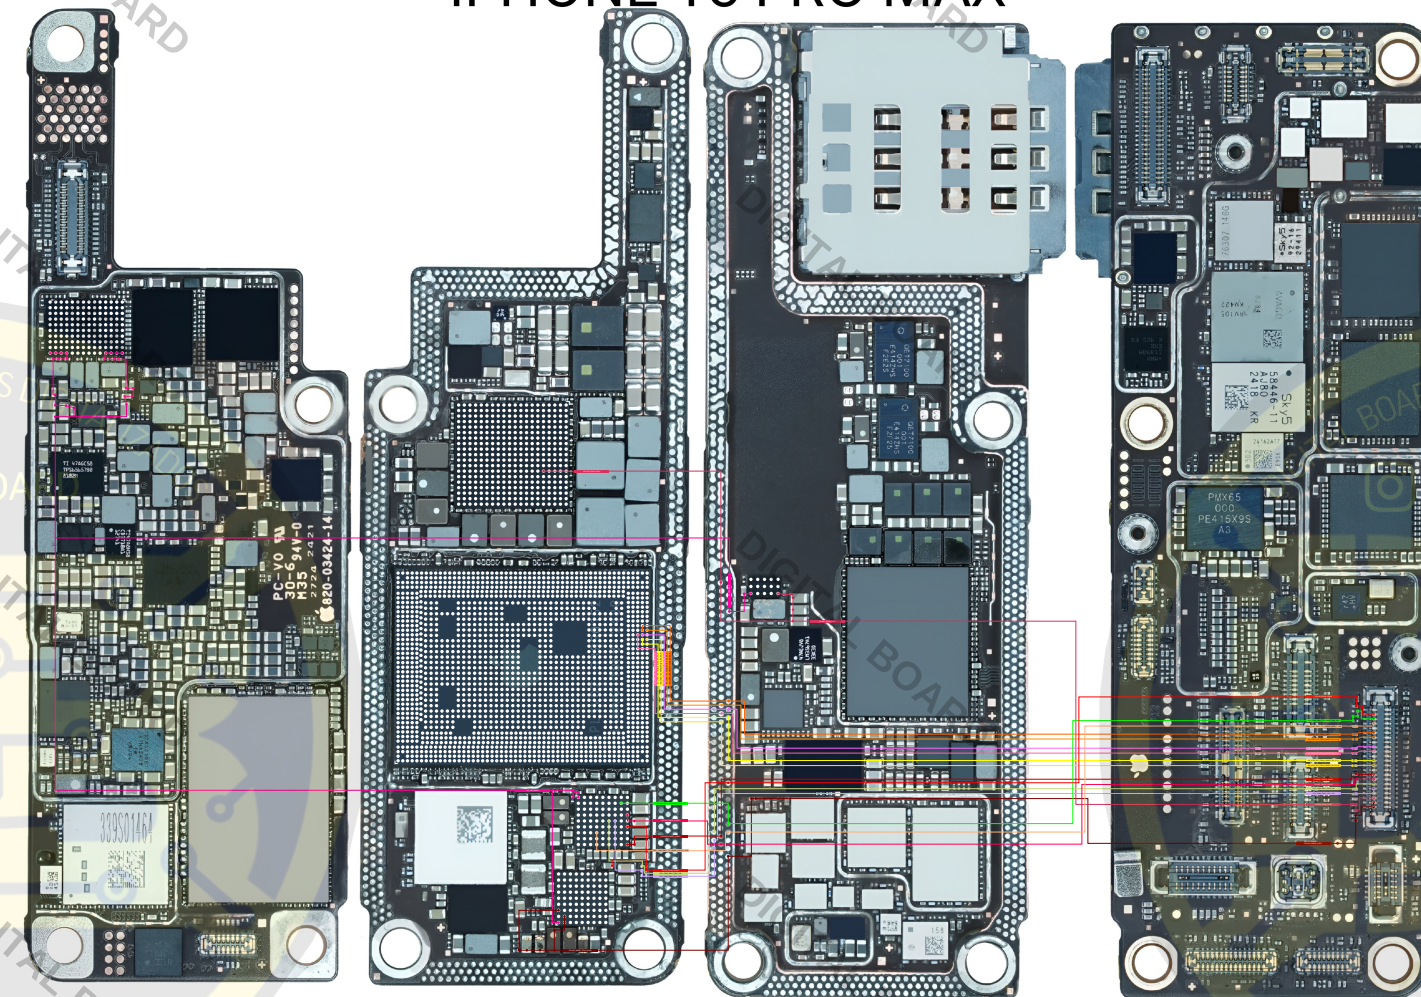

90\_LPDP\_ISP\_FROM\_SWIDE\_RX\_D0\_P  
90\_LPDP\_ISP\_FROM\_SWIDE\_RX\_D0\_N  
90\_LPDP\_ISP\_FROM\_SWIDE\_RX\_D1\_P  
90\_LPDP\_ISP\_FROM\_SWIDE\_RX\_D1\_N  
90\_LPDP\_ISP\_FROM\_SWIDE\_RX\_D2\_P  
90\_LPDP\_ISP\_FROM\_SWIDE\_RX\_D2\_N

CLK\_CAM\_PMU1\_TO\_SWIDE\_24M\_1V8  
GPIO\_CAM\_PMU1\_TO\_SWIDE\_SHDN\_L\_1V8  
I2C1\_CAM\_PMU1\_SCL\_1V8  
I2C1\_CAM\_PMU1\_SDA\_1V8

PP1V8\_RCAM\_VDDIO  
PP2V925\_SWIDE\_AVDD1  
PPVAR\_SWIDE\_AVDD2  
PPVAR\_RCAM\_PVDD  
PPVAR\_SWIDE\_DVDD  
PP\_VDD\_MAIN