


IP 16PRO MAX

TOF 3D LIDAR

DIGITAL BOARD ESQUEMAS DIGITALIZADOS

IPHONE 16 PRO MAX

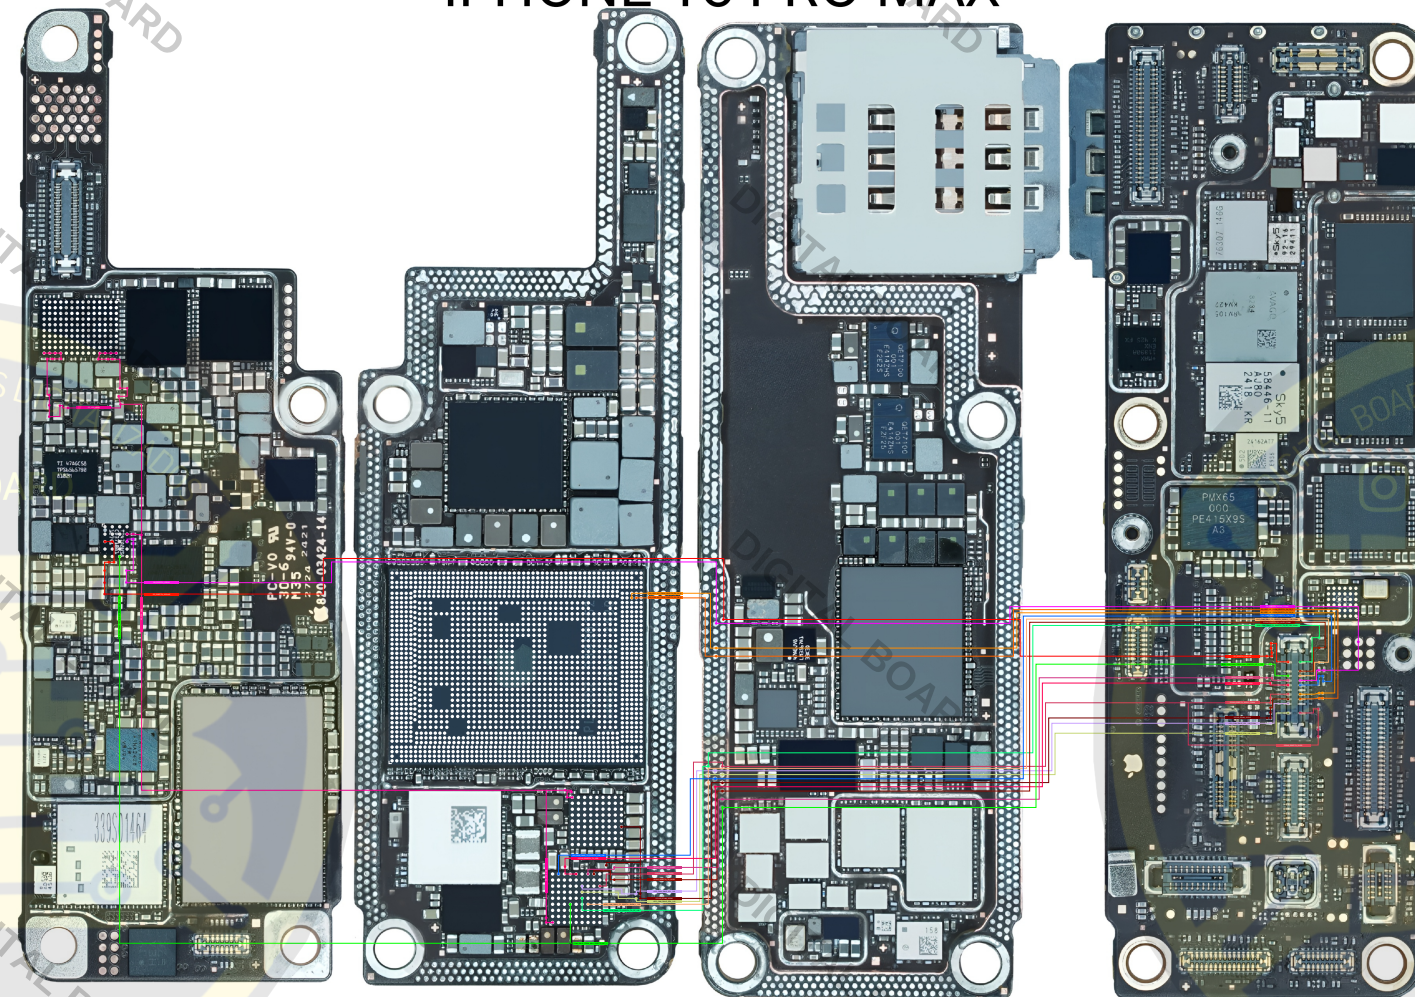

90_LPDP_ISP_FROM_RDEPTH_RX_D0_CONN_P
90_LPDP_ISP_FROM_RDEPTH_RX_D0_CONN_N
GPIO_CAM_PMU2_TO_RDEPTH_TX_CE_1V8_CONN
CLK_CAM_PMU2_TO_RDEPTH_12M_1V8_CONN
I2C2_CAM_PMU2_SCL_1V8_CONN

GPIO_CAM_PMU2_TO_RDEPTH_SHDN_L_1V8_CONN
GPIO_CAM_PMU2_FROM_WILL_RDEPTH_INT_L_1V8
I2C2_CAM_PMU2_SDA_1V8_CONN
PP_VDD_MAIN
PN_RDEPTH_VDDH_V_CONN
PP_RDEPTH_VDDLAS_CONN

PP1V5_RDEPTH_TX_VDD
PP3V2_RDEPTH_TX_AVDD
PP3V0_RDEPTH_RX_AVDD_CONN
PP0V9_RDEPTH_VDDL2_CONN
PP1V8_RCAM_VDDIO