


IP 16PRO MAX

WIFI E BT

DIGITAL BOARD ESQUEMAS DIGITALIZADOS
IPHONE 16 PRO MAX

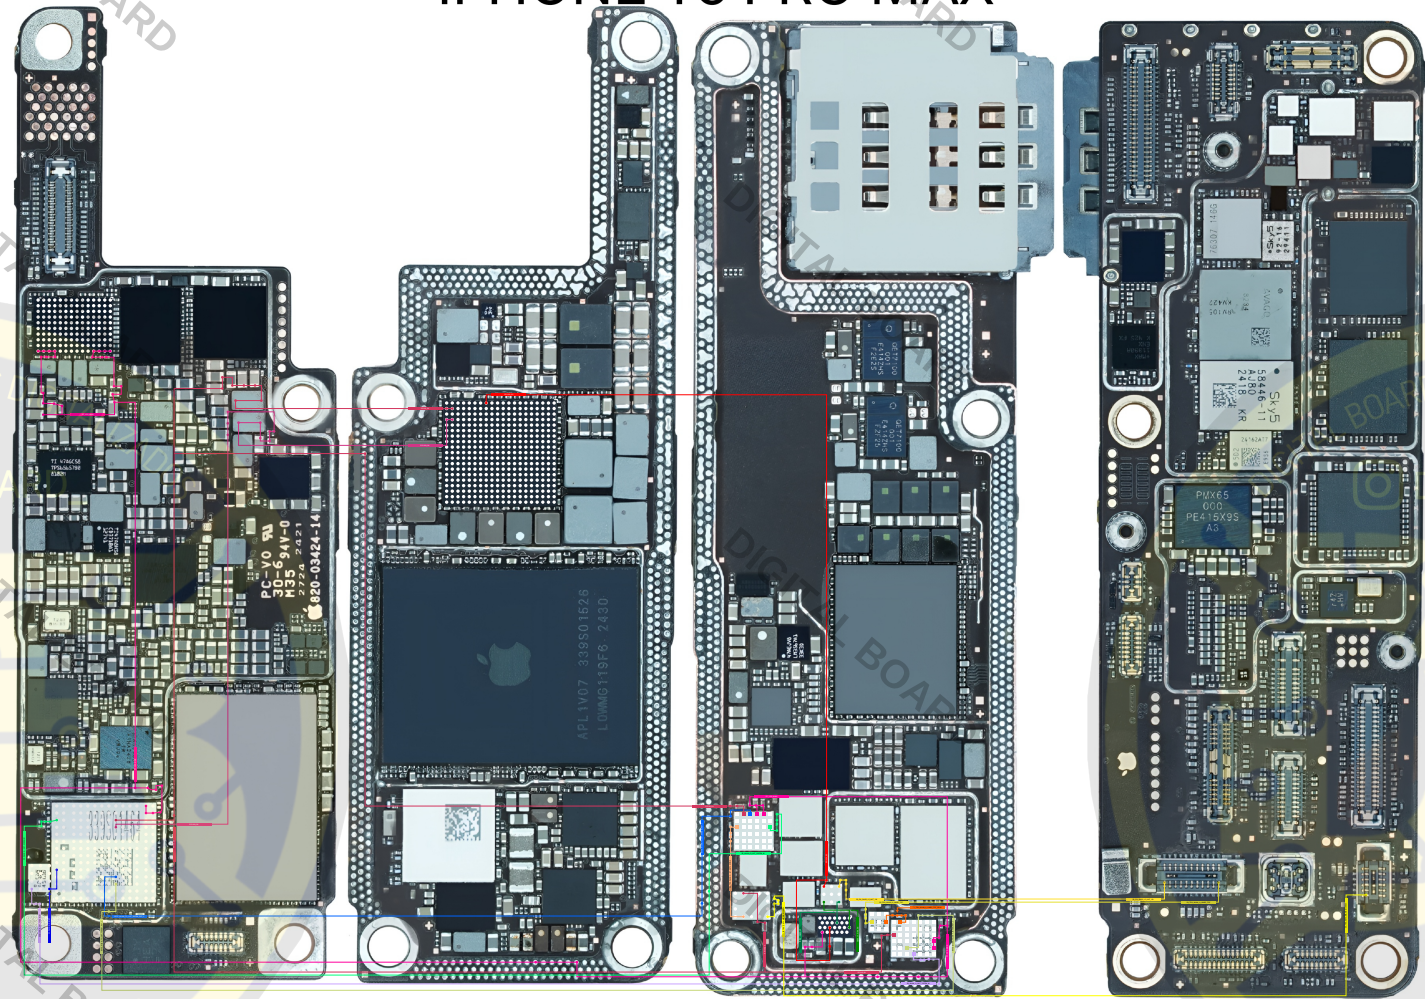

50_TRX_ANT4_MB_HB_WLAN24	RFFE_WLAN_TO_UAT_7GFEM_RST_L
50_TRX_WLAN_G_BT_ANT4_SWPLX	50_RX_GNSS_L5_ANT_10L
50_WLAN_G_UAT_2GFEM_M	50_RX_GNSS_L5
50_WLAN_A_C0_ISF	GNSS_L5_ELNA_EN
50_WLAN_A_UAT_7GFEM_M	PP1V8_S4
50_TRX_WLAN_A_UWB5_TOF_DPLX	PP1V24_S4
50_TRX_WLAN_A_UWB5_TOF	PP_VDD_MAIN
RFFE_WLAN_TO_UAT_2GFEM_RST_L	PP1V24_S2